


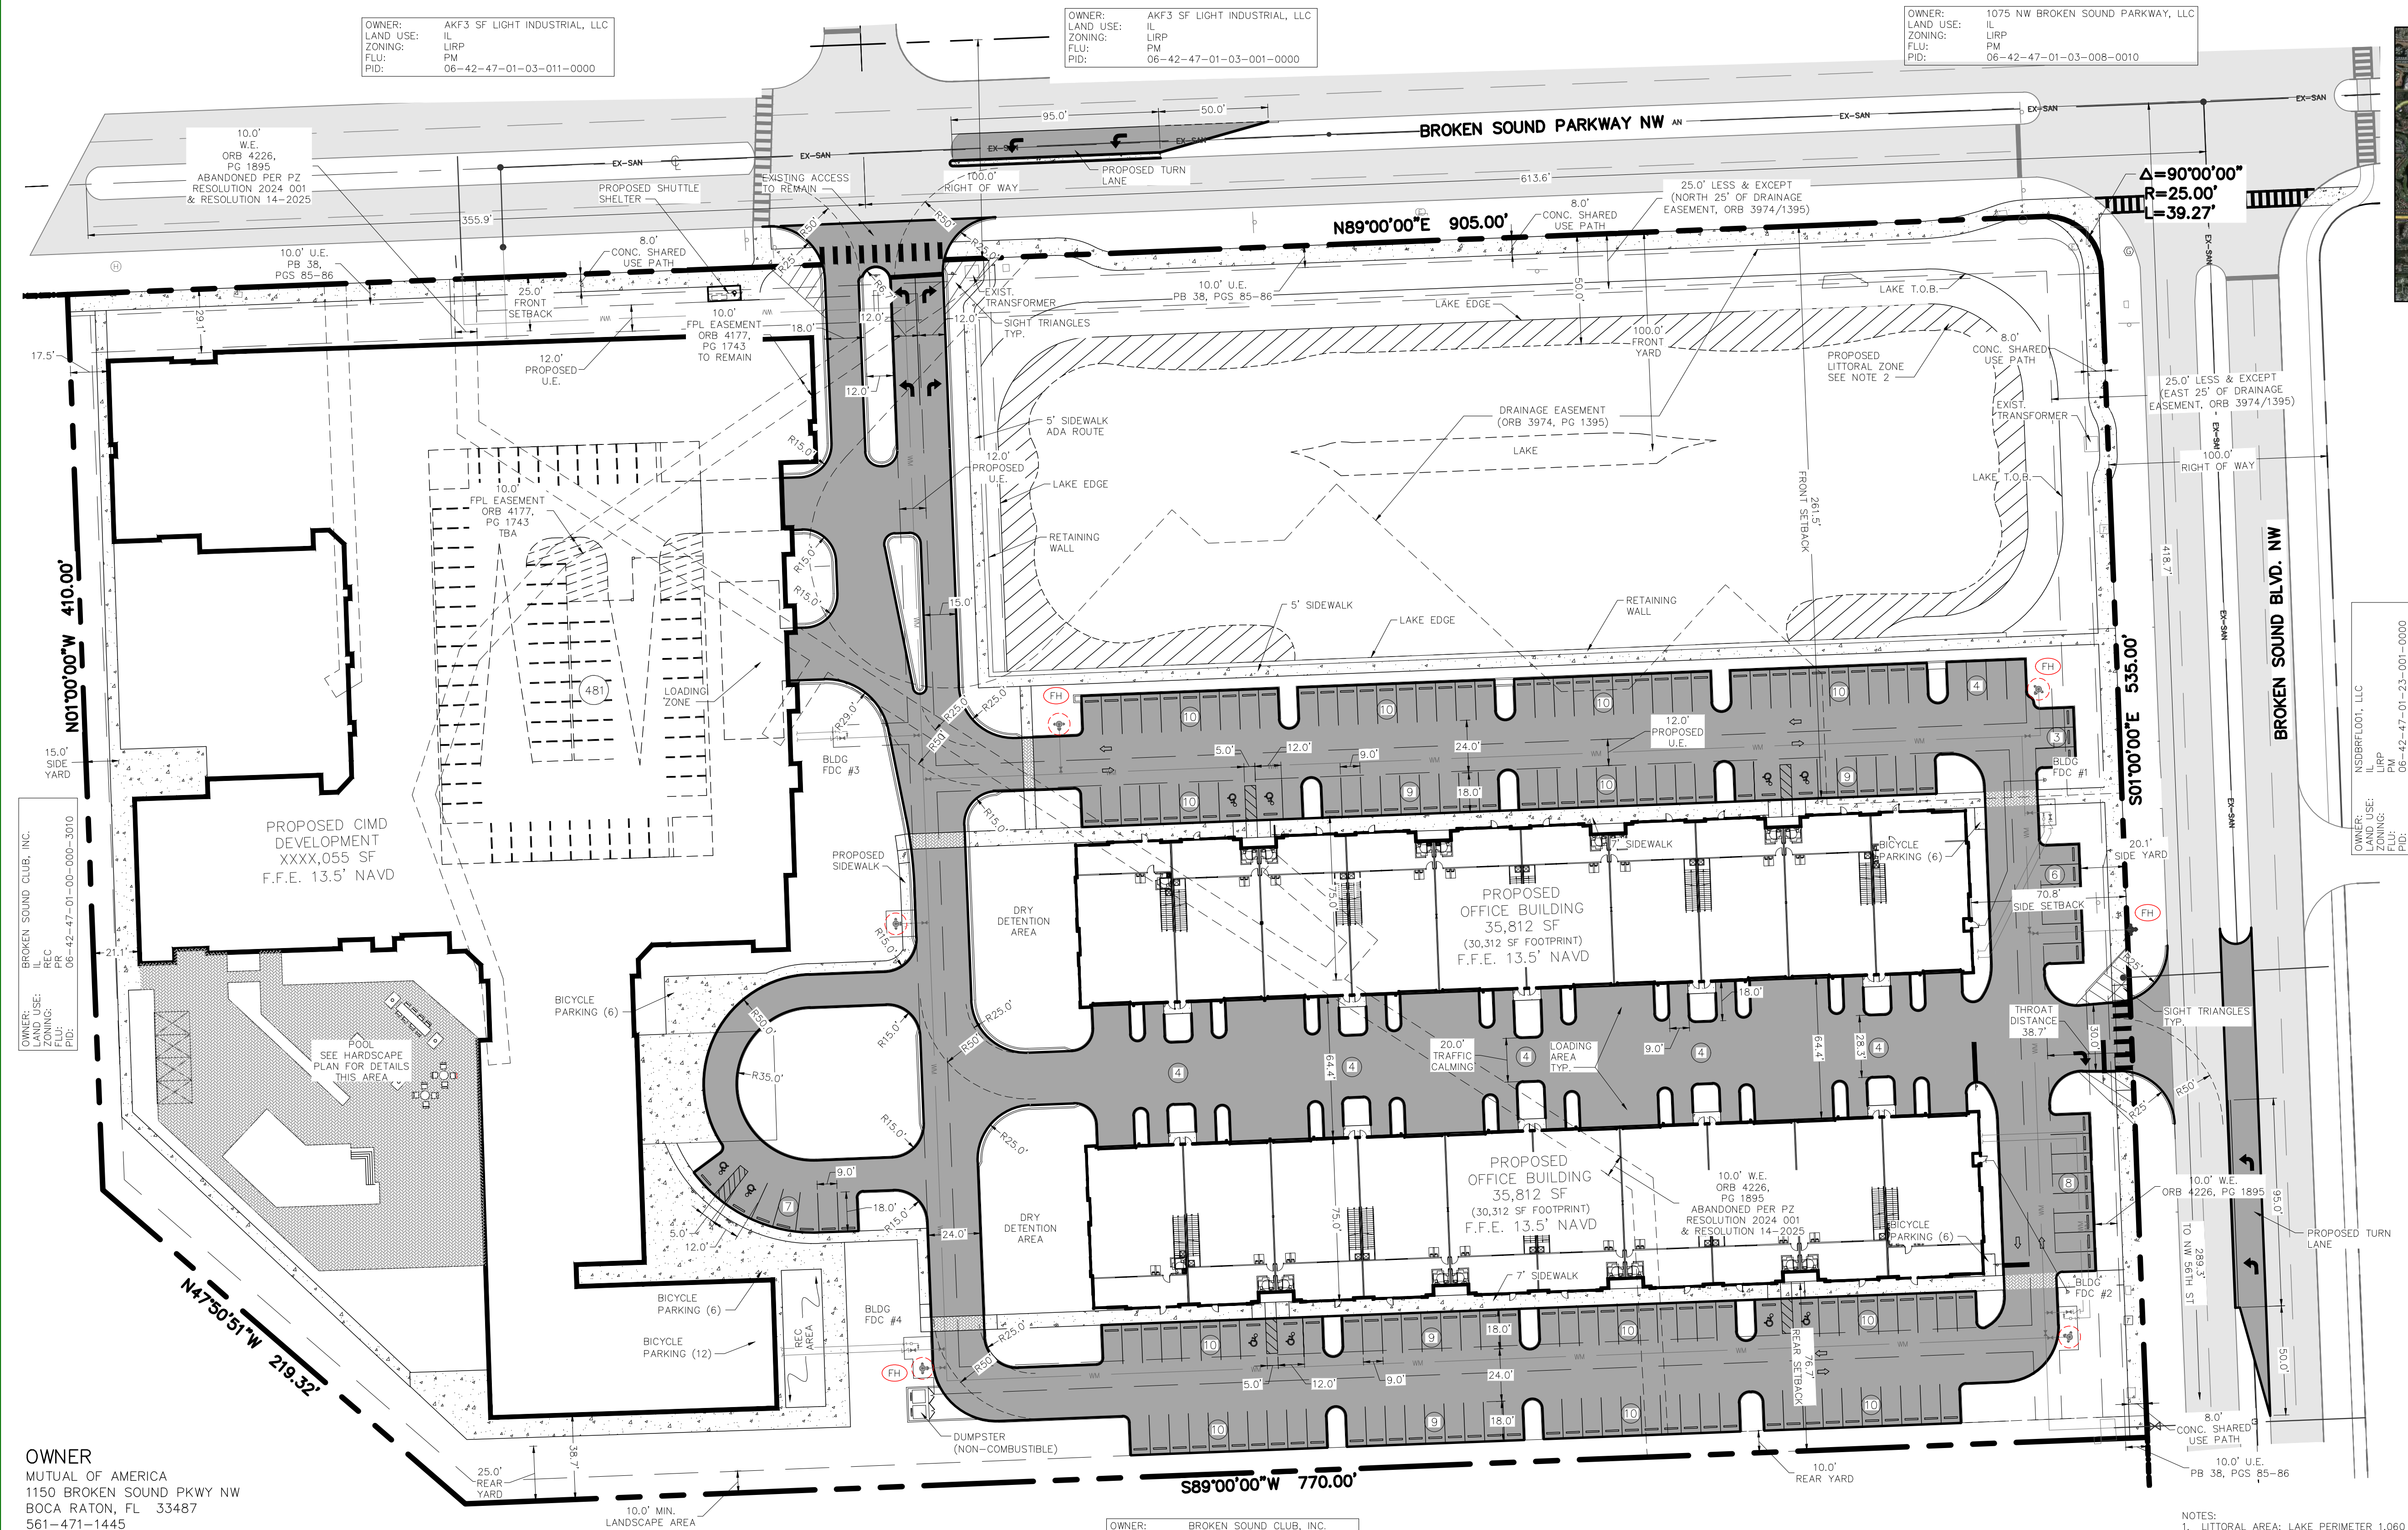

LOCATION MAP

TABULAR DATA

NAMES OF APPLICATION:	1150 INNOVATION CENTER 1150 BROKEN SOUND PKWY NW
OWNER:	1150 BROKEN SOUND, LLC
APPLICATION NO.:	PZSPA-2025-00026
LAST BCC APPROVAL:	N/A
TIER:	URBAN, SUBURBAN
EXISTING USE:	OFFICE
PROPOSED USE:	OFFICE/RESIDENTIAL
ZONING:	LIRP
FLU:	PM
SECTION/TOWNSHIP/RANGE:	56/1475/R43E
PROPERTY CONTROL NUMBERS:	06 42 47 01 04 002 0000
MAX. LOT COVERAGE:	(381,500 SF) 8.75 AC.
GROSS SITE AREA:	(508,667 SF) 11.677 AC.
PROPOSED COVERAGE: (FOOTPRINT)	
PROPOSED OFFICE BLDG	60,624 SF
APPROVED RESID. BLDG	52,580 SF
APPROVED RESID. GARAGE	23,413 SF
TOTAL	136,617 SF
PROPOSED COVERAGE	136,617/508,667 = 26.86%
(ALLOWABLE LOT COVERAGE 40%)	
ALLOWABLE GROSS FLOOR AREA	432,367 SF 9.926 AC.
PROPOSED OFFICE BLDG **	71,624 SF 1.644 AC.
APPROVED RESID. BLDG	355,055 SF 8.151 AC.
FAR = 426,679 / 508,667 = 0.839 (ALLOWABLE FAR 1.0)	
IMPERVIOUS SURFACE AREA:	* 6.871 AC. 58.84%
OPEN SPACE AREA:	4.806 AC. 41.16%
* INCLUDES REC. GOLF AREA	
** INCLUDES MEZZANINE	

PARKING CALCULATION (71,624 SF)		
OFFICE		
1 PER 200 TO 4000 SF =	20	PROP.
1 PER 300 EXCESS SF (31,812 SF) =	106	106
	126	126
LIGHT INDUSTRIAL		
1 PER 500 SF (35,812 SF) =	72	68
TOTAL: (84+98=182*)	179*	194
* PER LIRP AMENDMENT		
ALLOWABLE 10% REDUCTION OF REQUIRED (90% REQ.)		
198 x 90% = 179 TOTAL REQUIRED		
HANDICAP 12'X18.5' PER ADA TABLE		
REQ. 6 PROP. 8		
BUILDING HEIGHT:		
MAX: 100' PROP. 35'		
BICYCLE PARKING:		
5% OF TOTAL: 164 SP X 5% =	9 SP REQUIRED	
10 SHORT TERM BICYCLE PARKING	10 SP PROVIDED	
RESIDENTIAL		
1.5 PER EFFICIENCY UNIT (2 UNITS)	3	REQ. PROP.
1.75 PER 1 BR UNIT (121 UNITS)	212	20
2 PER 2 BR UNIT (131 UNITS)	262	106
2 PER 3 BR UNIT (33 UNITS)	66	126
TOTAL	543	
ALLOWABLE 10% REDUCTION ***		
(543 x 90% = 489 TOTAL REQ.)	489	502
HANDICAP 12'X18.5' 2% OF TOTAL		
REQ. 10 PROP. 10		
BUILDING HEIGHT:		
RESIDENTIAL 85' PROP. 67.7'		
BICYCLE PARKING:		
5% OF TOTAL: 543 SP X 5% =	27 SP REQUIRED	
36 BICYCLE PARKING PROVIDED ON GROUND		
*** WORKFORCE HOUSING UNITS: 15		
AFFORDABLE UNITS: 29		
OFFICE: 44		
FEMA DATA:		
BASE FLOOD EL. BASED ON FIRM MAP 12099C09860		
OFFICE: 10.5' NAVD		
RESIDENTIAL: 11.0' NAVD		
DESIGN FLOOD ELEVATION: 12.6' NAVD		
MIN. F.F.E. SFWMD: 12.5' NAVD		
CENTER ROAD EL. + 1.5'	13.2' NAVD	
SET F.F.E. (ALL BLDGS)	13.5' NAVD	

- NOTES:
- LITTORAL AREA; LAKE PERIMETER 1,060 LF; AREA REQUIRED 10,600 SF; 11,870 SF PROVIDED
 - FIRE SERVICE APPLIANCES - EDCS; HYDRANTS, BACKFLOW DEVICES, ETC. SHALL HAVE A MINIMUM OF 5 FT OF CLEARANCE ON ALL SIDES AND FROM OVERHEAD.
 - DUMPSTER ENCLOSURES SHALL NOT BE PLACED WITHIN 10 FT OF COMBUSTIBLE WALLS, OPENINGS, OR COMBUSTIBLE ROOF EAVE LINES.
 - LANDSCAPING SHALL NOT BE PLANTED OVER FIRE SERVICE WATER MAINS OR PROHIBIT ACCESS TO FIRE SERVICE APPLIANCES. REFER TO THE CITY OF BOCA RATON CODE OF ORDINANCES - CHAPTER 7 FIRE CODE, AND THE FFPC FOR COMPLIANCE AND ADDITIONAL REQUIREMENTS. PROVIDE NOW, OR UPON PERMIT SUBMITTAL, VERIFICATION OF CONTRACTOR'S LICENSE TO PERFORM FIRE MAIN UNDERGROUND WORK/INSTALLATION PER FS 633.
 - SIDEWALK ALONG ROAD RIGHT OF WAY MAY HAVE FIELD ADJUSTMENTS DUE TO EXISTING TREES. EASEMENTS WILL BE PROVIDED FOR SIDEWALKS OUT SIDE OF RIGHT OF WAY.

OWNER
MUTUAL OF AMERICA
1150 BROKEN SOUND PKWY NW
BOCA RATON, FL 33487
561-471-1445
WWW.MUTUALOFAMERICA.COM

DEVELOPER
1150 BROKEN SOUND, LLC
6820 LYONS TECHNOLOGY CIR STE 100
COCONUT CREEK, FL 33073
954-312-2400
INFO@BUTTERS.COM

SURVEYOR
AVIROM & ASSOCIATES, INC.
50 SW 2ND AVENUE, SUITE 102
BOCA RATON, FL 33432
561-392-2594
INFO@AVIROMSURVEY.COM

ENGINEER
SMILEY & ASSOCIATES, INC.
624 KINGFISH ROAD
NORTH PALM BEACH, FL 33408
561-596-0562
MSMILEY@SMILEY-ASSOCIATES.COM

ARCHITECT
CMBE ARCHITECTURE
7601 N. FEDERAL HWY., STE B205
BOCA RATON, FL 33487
561-233-9999
CARLO@CMBEARCHITECTURE.COM

WATER & SEWER FLOWS			
APPROVED:	71,624 SF	0.1 GPD/SF	7,162 GPD
STORAGE:	71,624 X 0.1 =		
PROPOSED:			
RESIDENTIAL UNITS:	2 X 100 GPD	=	200 GPD
EFFICIENCY UNITS	121 X 100 GPD	=	12,100 GPD
1 BR UNITS	131 X 200 GPD	=	26,200 GPD
2 BR UNITS	33 X 300 GPD	=	9,900 GPD
3 BR UNITS			
TOTAL:			55,562 GPD
EXISTING: (CREDIT)			
GENERAL OFFICE:	64,708 SF	15 GPD/100 SF	
	64,708/100 = 647.08 X 15 =	9,706.2 GPD	
INCREASE OF 45,855.8 GPD			

SETBACKS (OFFICE BUILDING)			
FRONT REQ/PROVIDED	REAR REQ/PROVIDED	SIDE STREET REQ/PROVIDED	INTERIOR SIDE REQ/PROVIDED
25'/261.5'	25'/84.2'	15'/100.2'	15'/420.2'

SETBACKS (RESIDENTIAL BUILDING)			
FRONT REQ/PROVIDED	REAR REQ/PROVIDED	SIDE STREET REQ/PROVIDED	INTERIOR SIDE REQ/PROVIDED
25'/44.2'	25'/30.1'	15'/622.1'	15'/34.7'



624 KINGFISH ROAD, NORTH PALM BEACH, FLORIDA 33408
561-596-0562 • msmiley@smiley-associates.com
www.smiley-associates.com
EB # 0613

DRT	DRT
DSG	MS
CHK	MS
CADDWG MA	

REV. DESCRIPTION

APRV DATE

REVISION NOTES

1150
INNOVATION CENTER
FOR
1150 BROKEN SOUND, LLC
BOCA RATON, FLORIDA

SITE PLAN

DIGITAL SEAL DATE 10/10/25

SP

SHEET TYPE

SHEET 1 OF 1

JOB # 25-003